


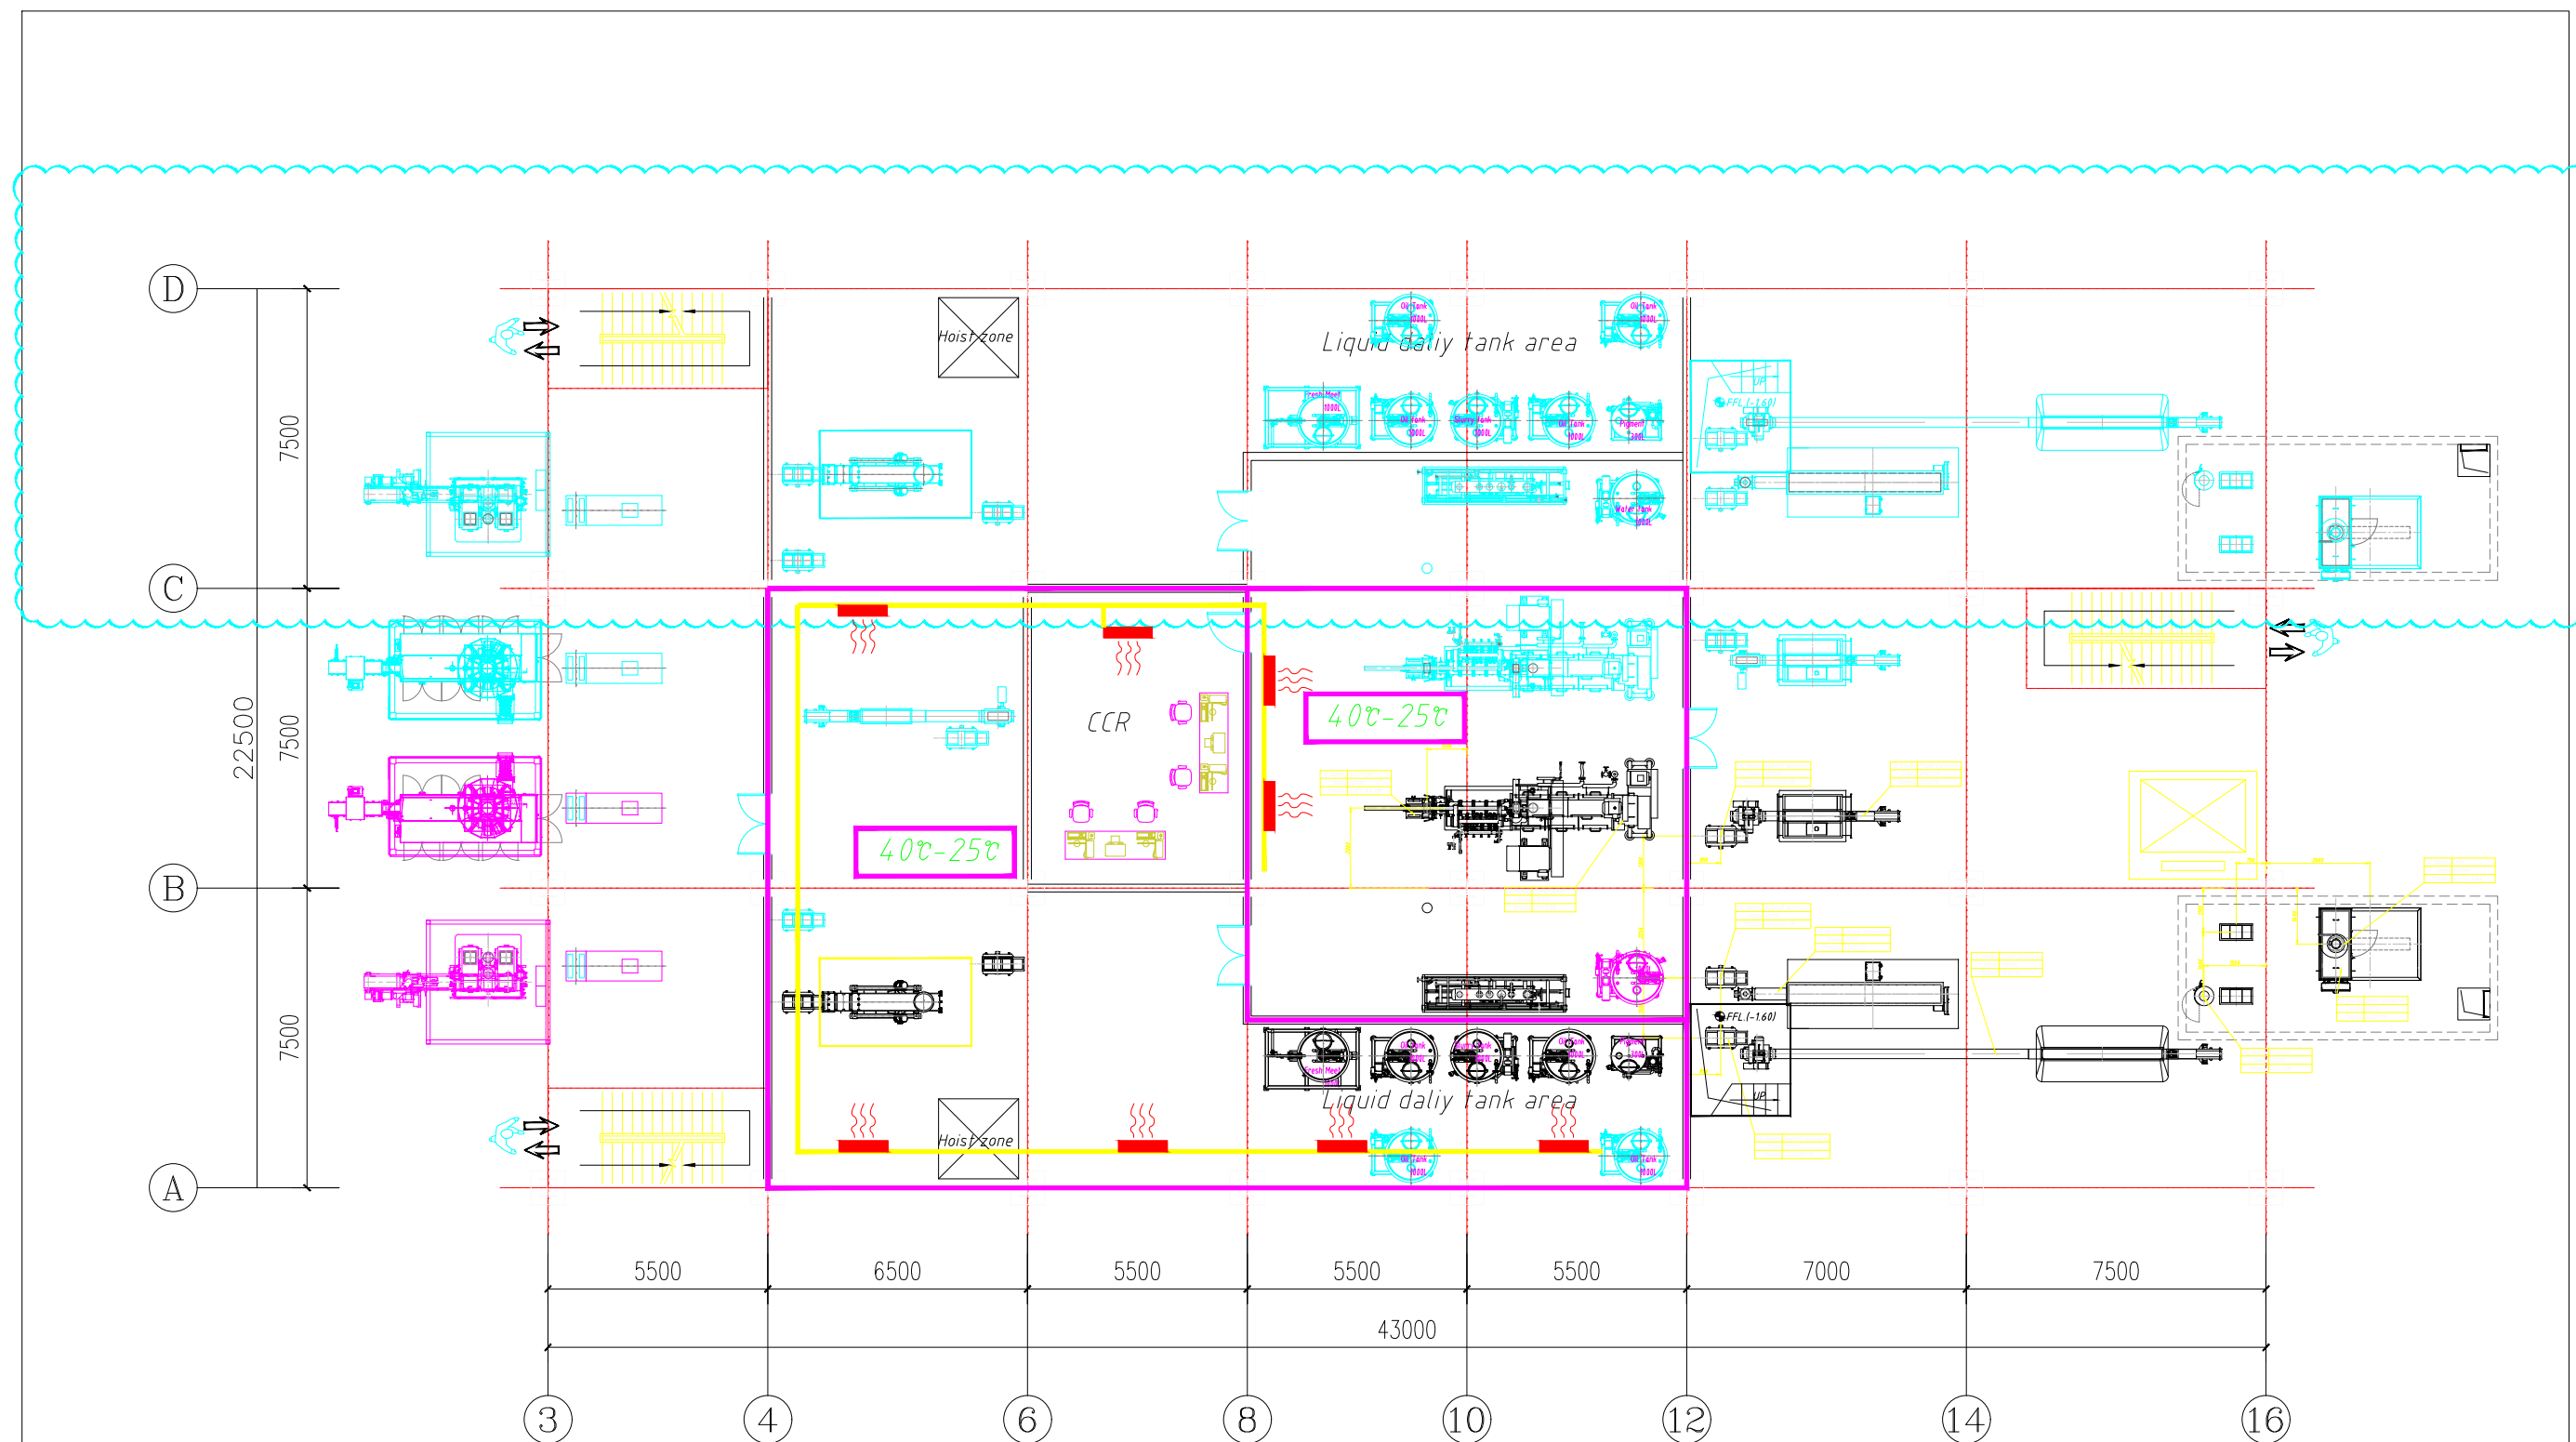

从主机出主管道DN150
 循环出水泵前后DN150
 变径到各楼层DN100（竖管）
 到末端水平管DN65
 接风机盘管DN32

FP-238风机盘管8台

PLAN VIEW ±0.00M

FAMSUN 江苏丰尚智能科技有限公司		建设单位 Client	PET FACTORY	
Integrated solution for petfood processing		项目名称 Project	5T/H pet food product line	
设计 Designer	???	审定 Checker	PLAN VIEW ±0.00M	
制图 Drawer		审核 Reviewer		
校核 Audit		设计号 Des NO.		
日期 Date	2011-11-11	比例 Scale		
				设计阶段 Stage
				图别 Grade
				图号 Draw NO.
				版本号 Ver NO.
				方案/细化
				工号
				GY-02
				1