



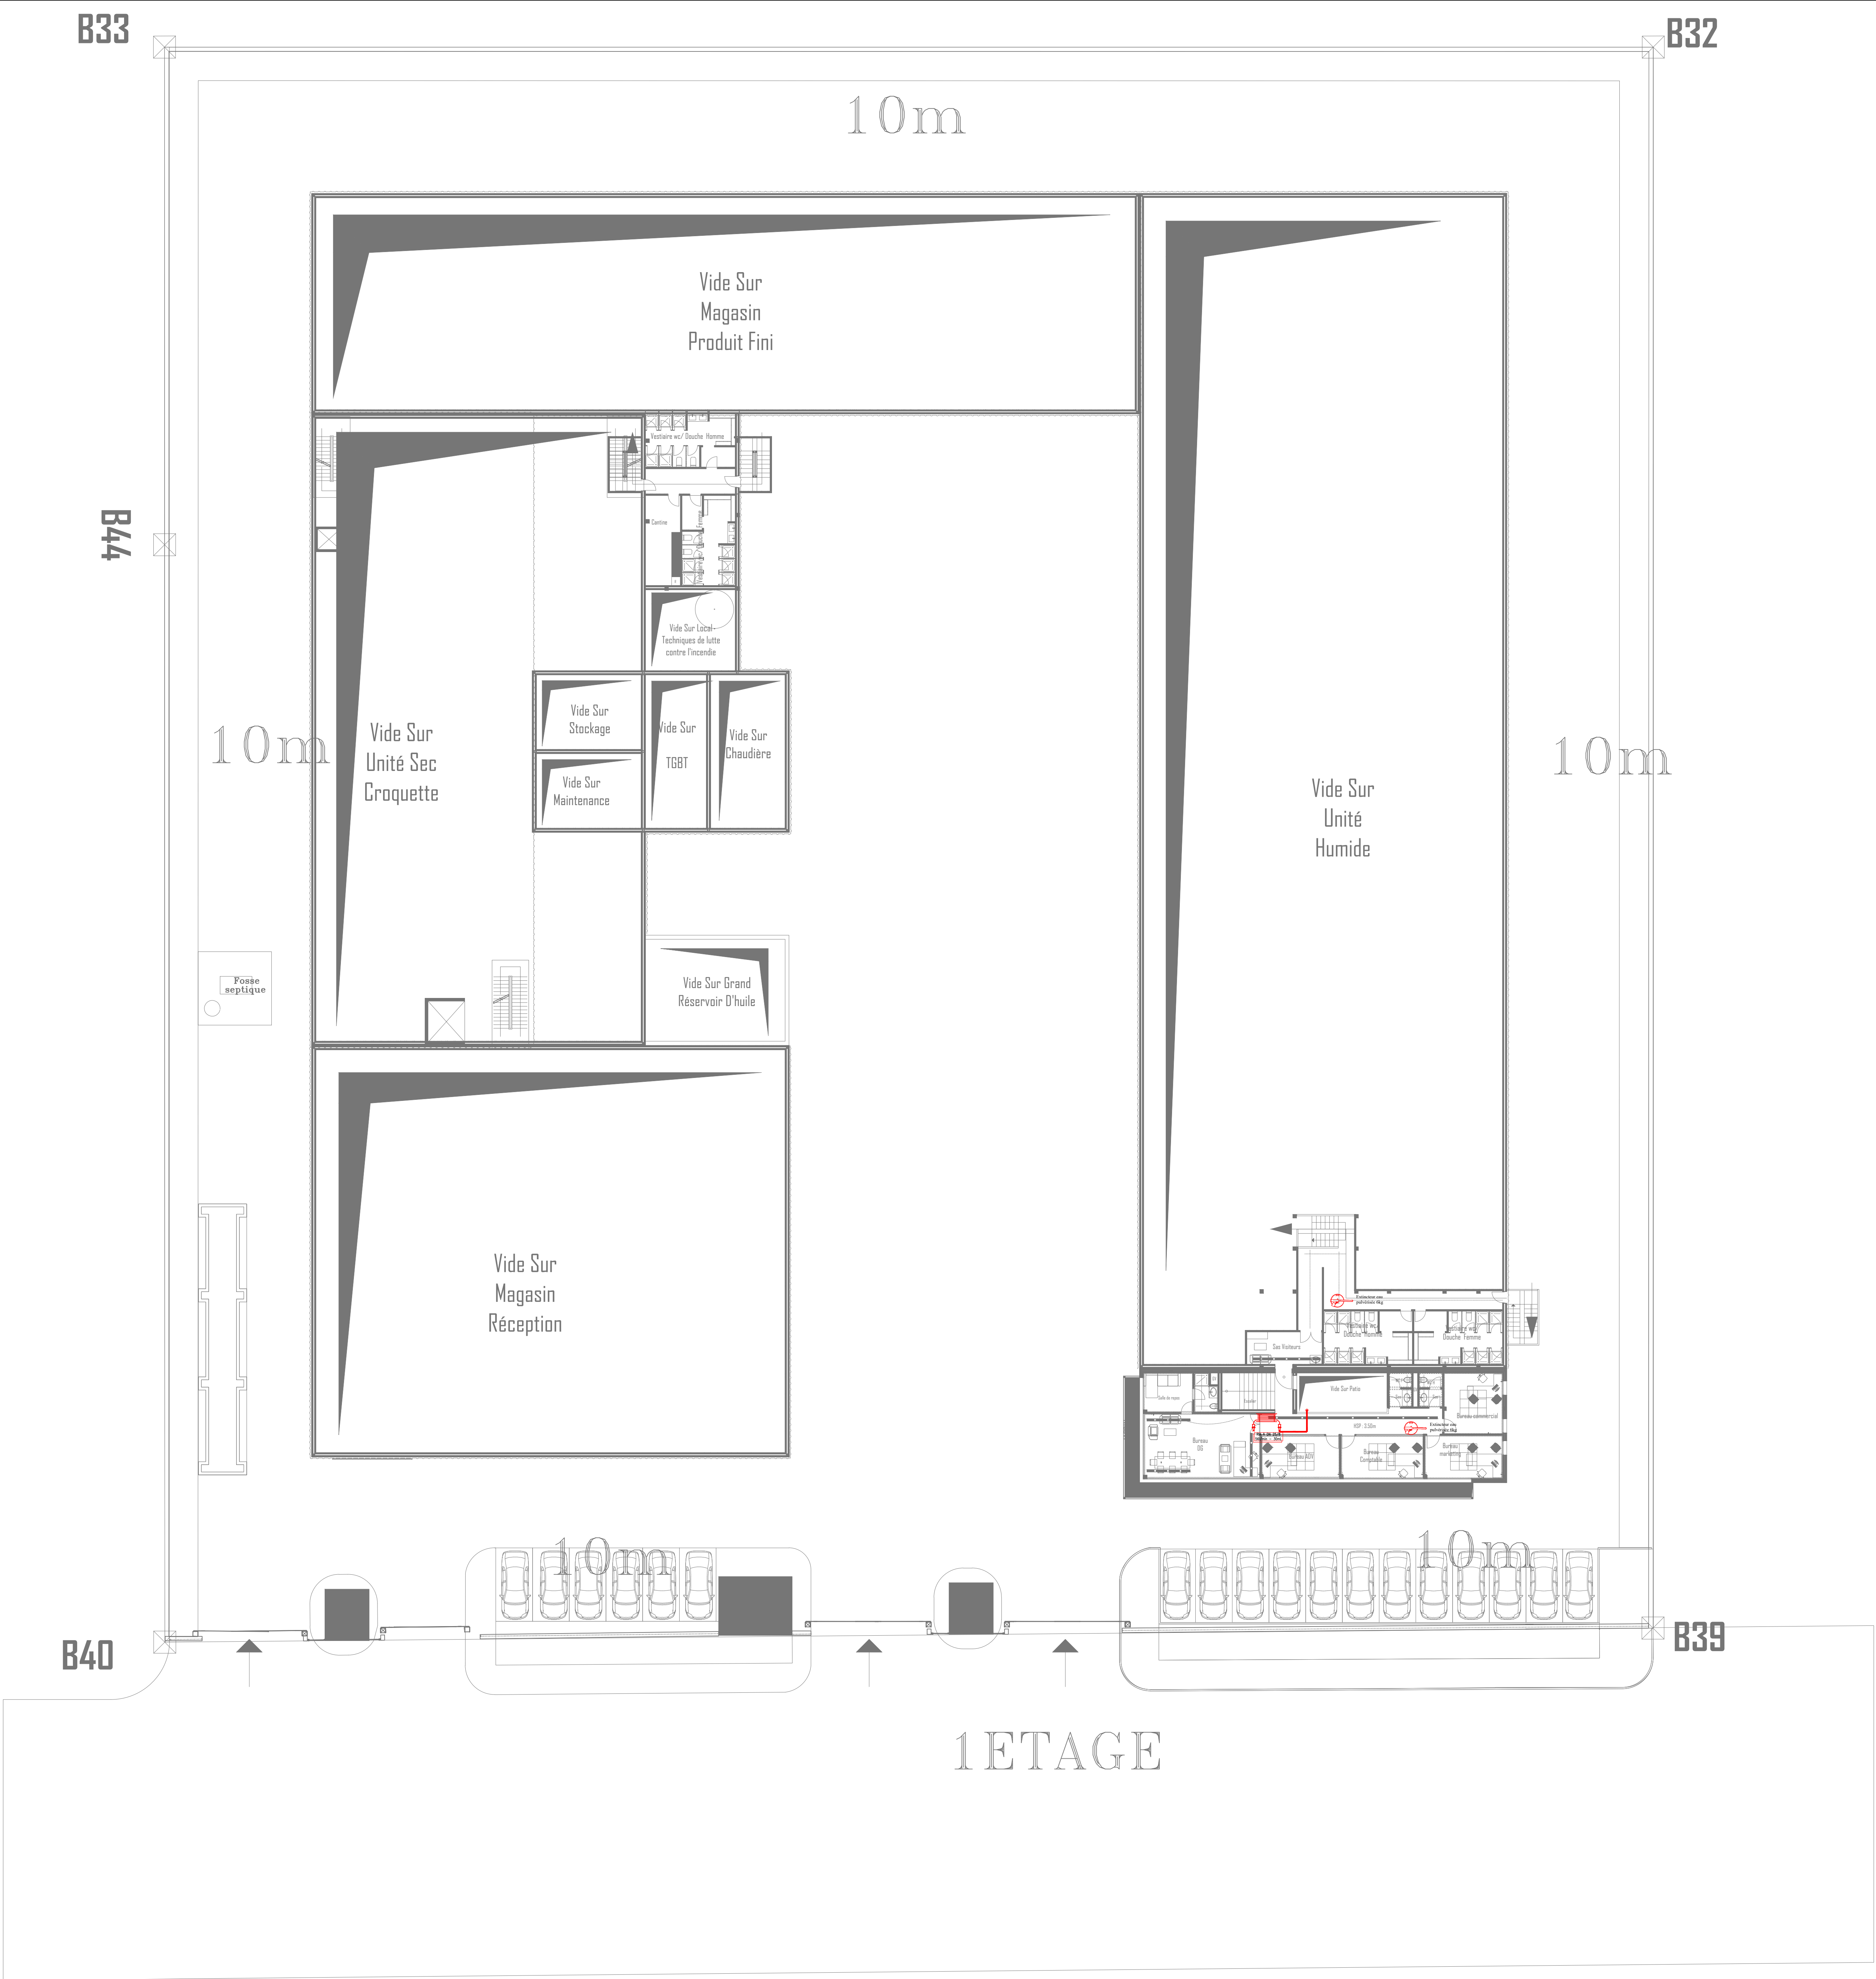

La légende

	EXTINCTEUR
	ROBINET D'INCENDIE ARME DEUX JETS
	TUYAU ACIER GALVANISE
	BAC A SABLE

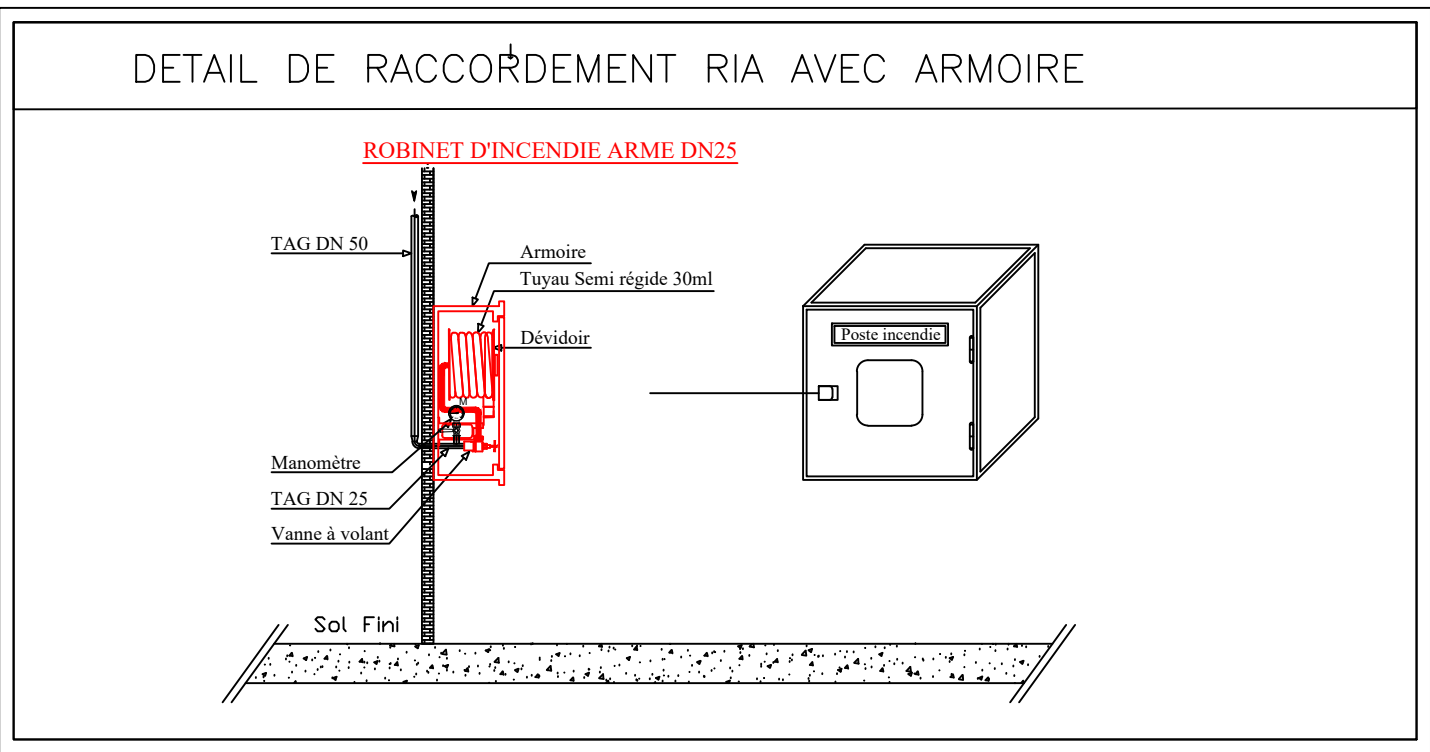

DN de la canalisation en fonction du nombre et des Ø du R.I.A et de l'orifice du diffuseur

LEGENDE MATERIELS / RESEAUX	
	R.I.A Robinet d'Incendie Armée DN 25
	Réseaux de distribution des postes RIA (TAG)
NB : Tube acier galvanisé trif 3 pour les diamètre inférieurs à 50/60 en tube tarif 10 au-dessus	

TABLEAU 3 de la Règle APSAD R5

Canalisation DN	Nombre de R.I.A		
	Ø 19/6 mm	Ø 25/8 mm	Ø 33/12 mm
40/49	≤ 4	≤ 2	–
50/60	≤ 8	≤ 4	≤ 2
66/76	≤ 12	≤ 12	≤ 6
80/90	> 24	> 12	> 6

MAITRE D'OUVRAGE



AUTEUR DU DOCUMENT



Angle avenues hassan II ,Rue abdou
Résidence hamza 3 ème étage - appt 7
kenitra
Tél : 0537 32 57 85
Email : ingenios@ ingenios.ma

Projet :

Projet de construction aménagement et équipement d'une usine de production d'aliments
d'animaux domestiques

Désignation :

PLAN PROTECTION D'INCENDIE -1-ER ETAGE-

Ech:

Lot:

Date :

Indice : A

Folio n° : FOL