



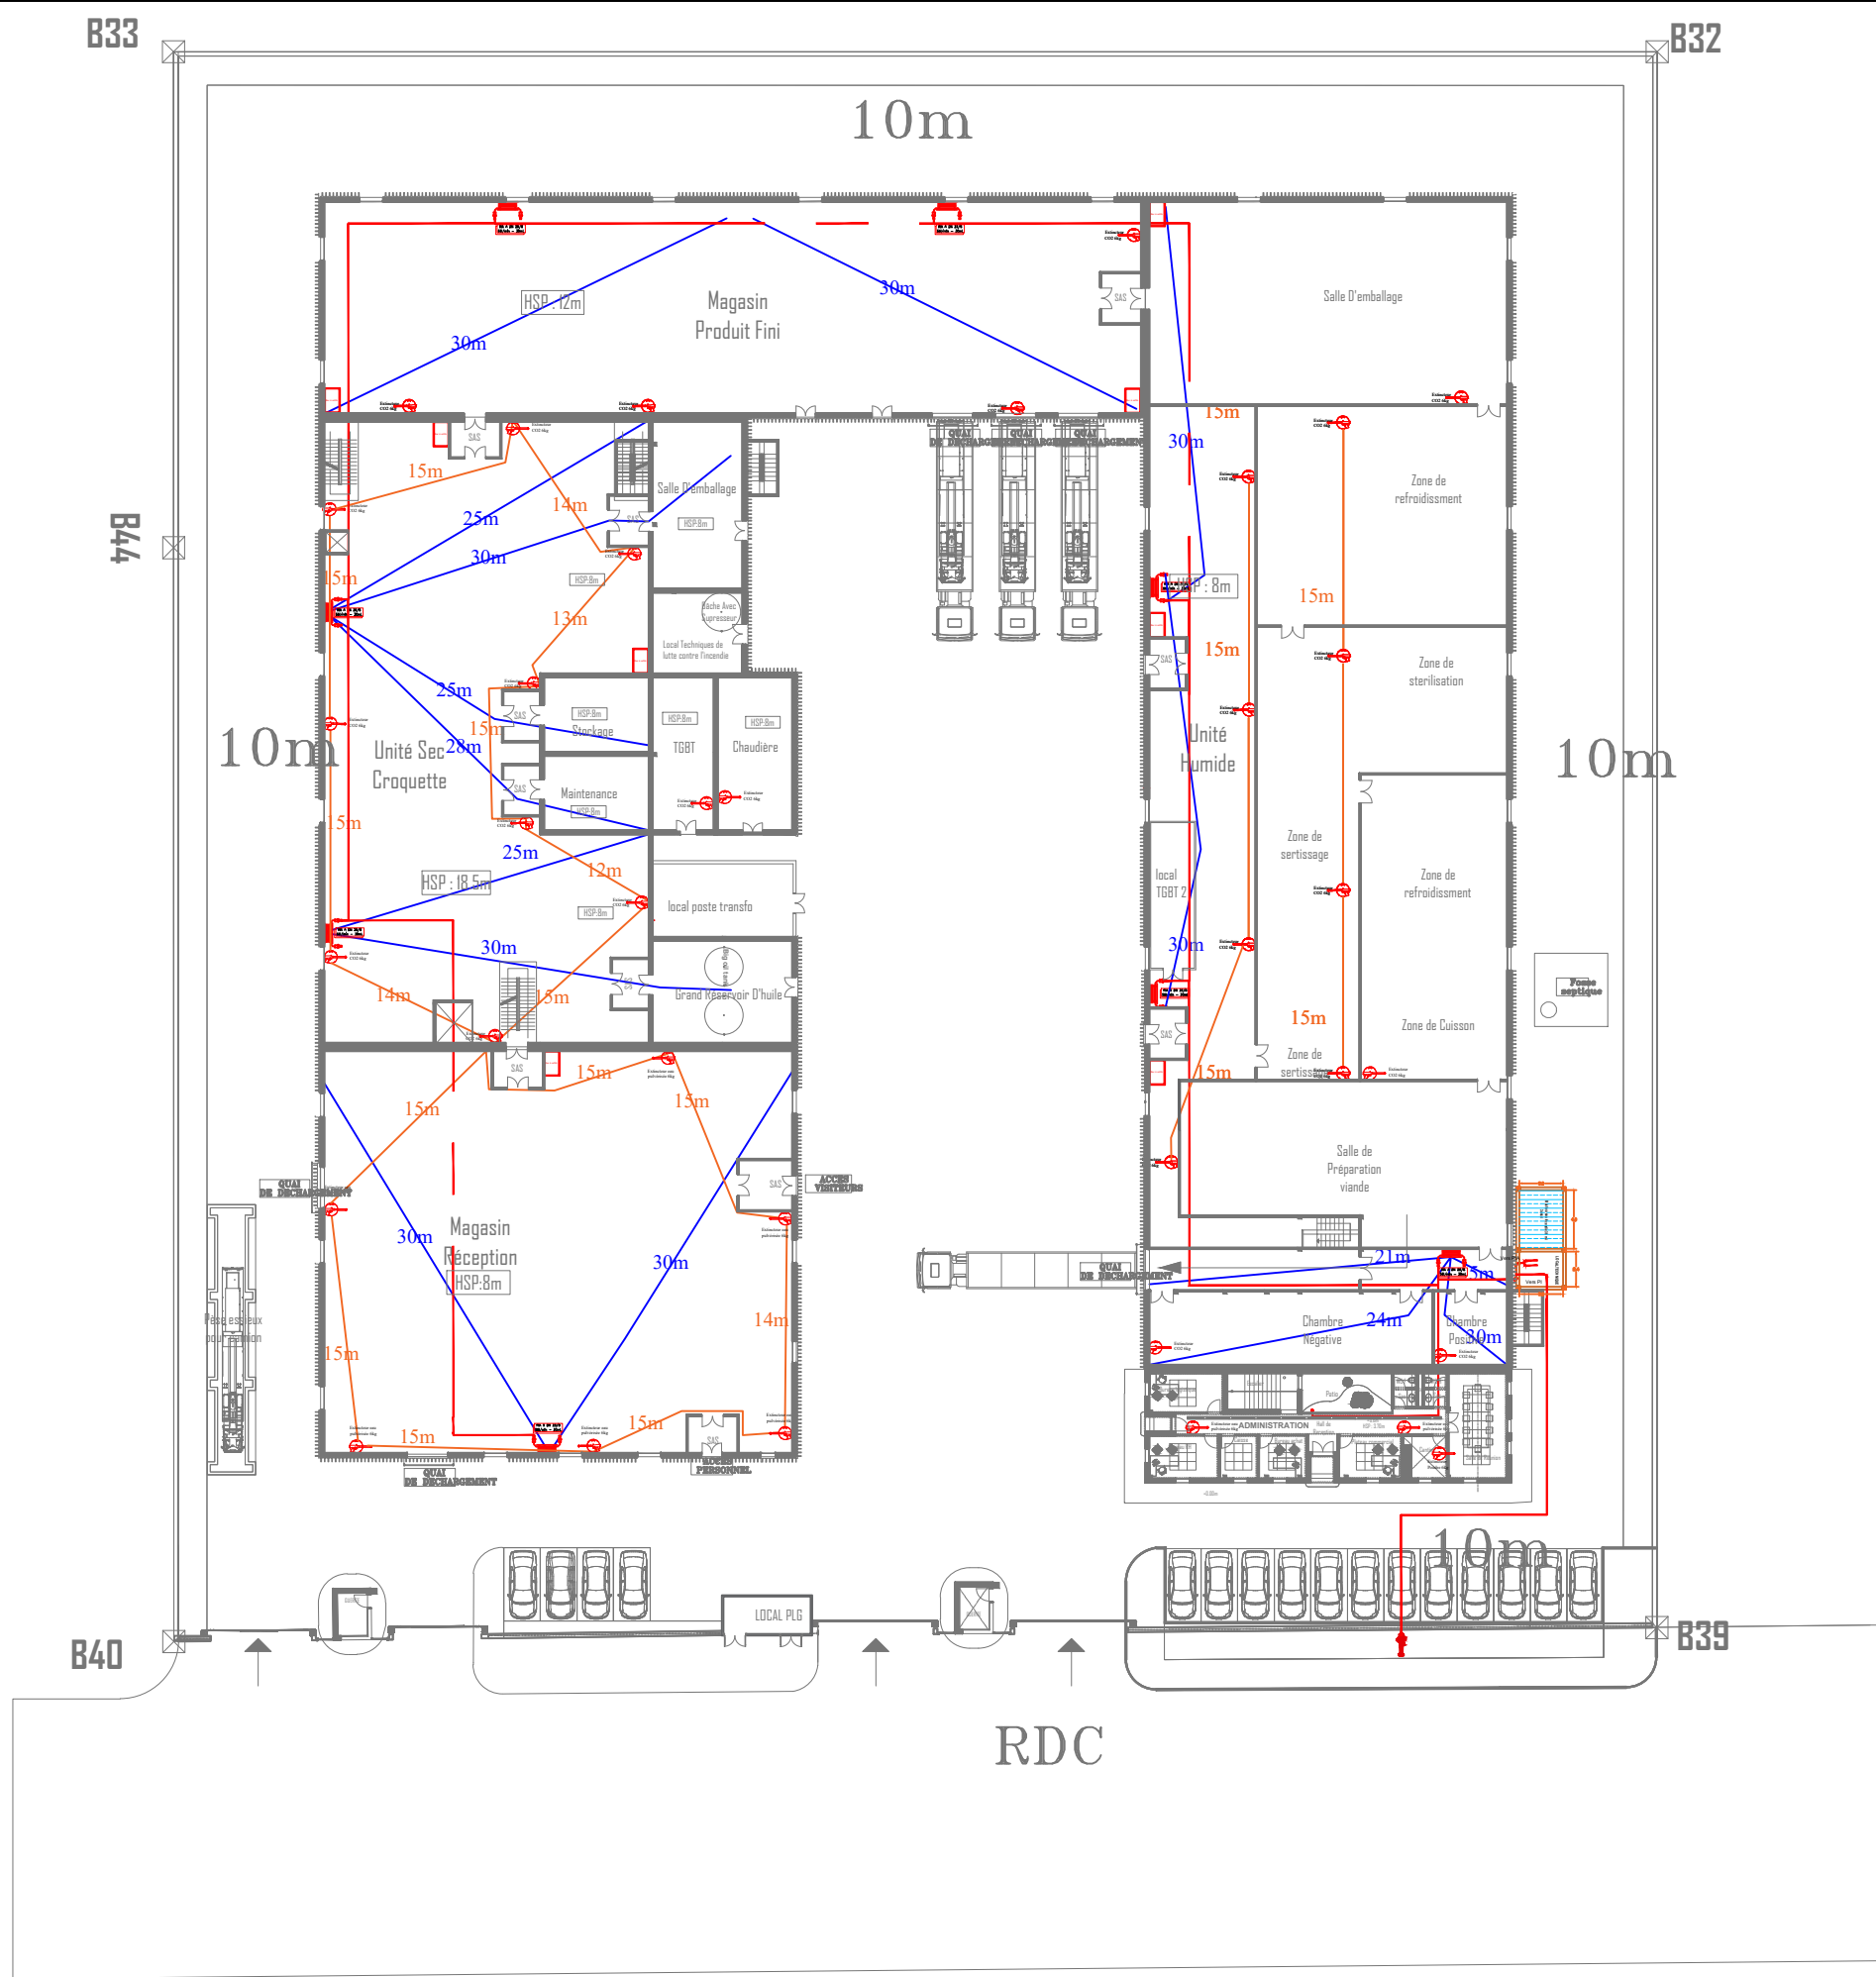

La légende

|  |                                   |
|--|-----------------------------------|
|  | EXTINCTEUR                        |
|  | ROBINET D'INCENDIE ARME DEUX JETS |
|  | TUYAU ACIER GALVANISE             |
|  | BAC A SABLE                       |

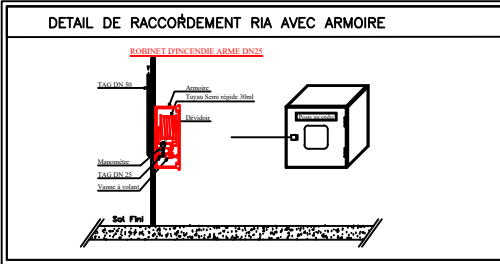

DN de la canalisation en fonction du nombre et des Ø du R.I.A et de l'orifice du diffuseur

| LEGENDE MATERIELS / RESEAUX                                                                      |                                              |
|--------------------------------------------------------------------------------------------------|----------------------------------------------|
|                                                                                                  | R.I.A Robinet d'Incendie Armée DN 25         |
|                                                                                                  | Réseaux de distribution des postes RIA (TAG) |
| NB : Tube acier galvanisé trif 3 pour les diamètre inférieurs à 50/60 en tube tarif 10 au-dessus |                                              |

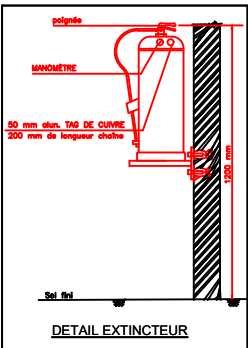


TABLEAU 3 de la Règle APSAD R5

| Canalisation<br>DN | Nombre de R.I.A |           |            |
|--------------------|-----------------|-----------|------------|
|                    | Ø 19/6 mm       | Ø 25/8 mm | Ø 33/12 mm |
| 40/49              | ≤ 4             | ≤ 2       | -          |
| 50/60              | ≤ 8             | ≤ 4       | ≤ 2        |
| 66/76              | ≤ 12            | ≤ 12      | ≤ 6        |
| 80/90              | > 24            | > 12      | > 6        |

MAITRE D'OUVRAGE



AUTEUR DU DOCUMENT



Angle avenues hassan II ,Rue abdou  
Résidence hamza 3 ème etage - appt 7  
kenitra  
Tél : 0537 32 57 85  
Email : ingenios@ ingenios.ma

Projet :

Projet de construction aménagement et équipement d'une usine de production d'aliments  
d'animaux domestiques

Désignation :

PLAN PROTECTION D'INCENDIE -RDC-

Ech:

Lot:

Date :

Indice : A

Folio n° : FOL