


SCHEMA SYNOPTIQUE SURPRESSEUR

PLAN STATION DE SURPRESSION
Bache à eau + Local Technique

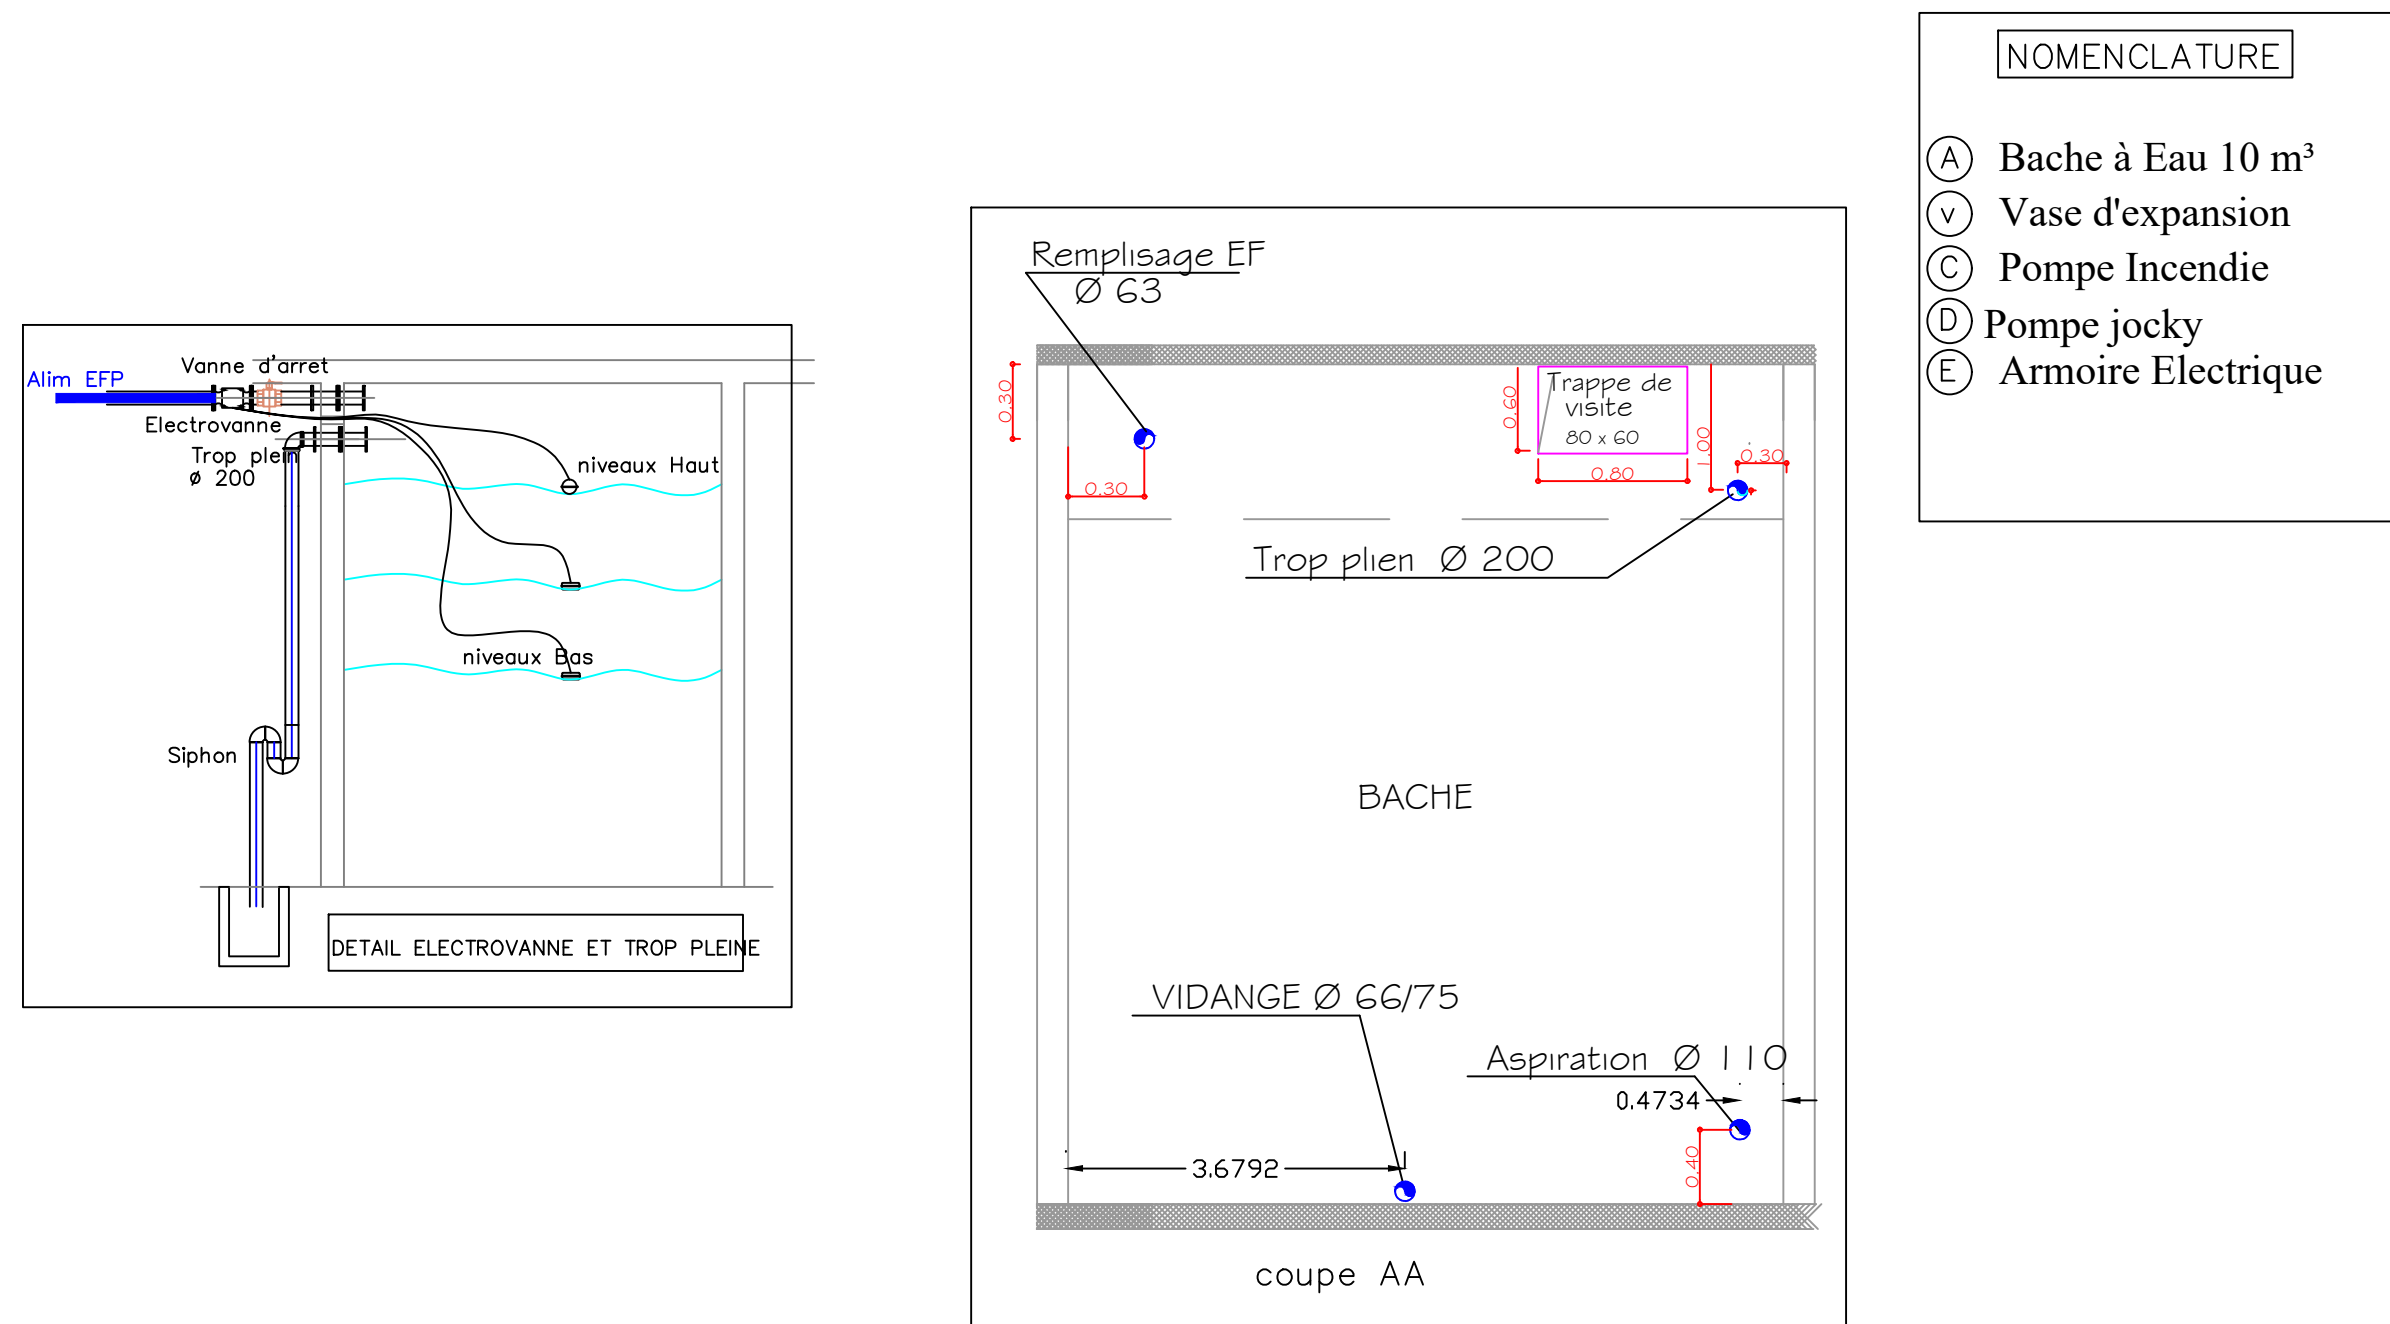

Remplissage bache à eau
PEHD - DN 63

By-pass
DN
Ø65

électrovanne

Remplissage

Bache incendie
Volume = 35m3

- DN100

- DN200

- DN150

un surpresseur d'incendie avec 1 pompes
jumelées pour le reseau de RIA

un surpresseur d'incendie avec 1 pompes
jumelées pour le reseau de PI

Vers PI

- DN80 Vers RIA

- DN100

- DN50

- DN50

- DN50

- DN50

- DN50

- DN50

MAITRE D'OUVRAGE



AUTEUR DU DOCUMENT



Angle avenues hassan II ,Rue abdou
Résidence hamza 3 éme etage - appt 7
kenitra
Tél : 0537 32 57 85
Email : ingenios@ ingenios.ma

Projet :

Projet de construction aménagement et équipement d'une usine de production d'aliments
d'animaux domestiques

Désignation :

SCHEMA SYNOPTIQUE SURPRESSEUR

Ech:

Lot:

Date :


Indice : A

Folio n° : FOL


LEGENDE




Vase d'expansion

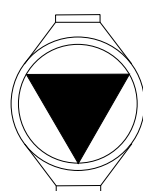

Pompe

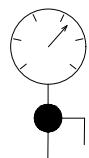


Manometre

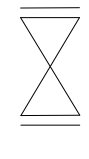


Vanne d'arret



Clapet anti-retour

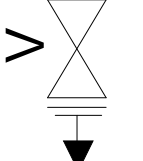

Vidange

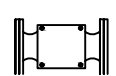

Electrovanne



manchette antivibratoire